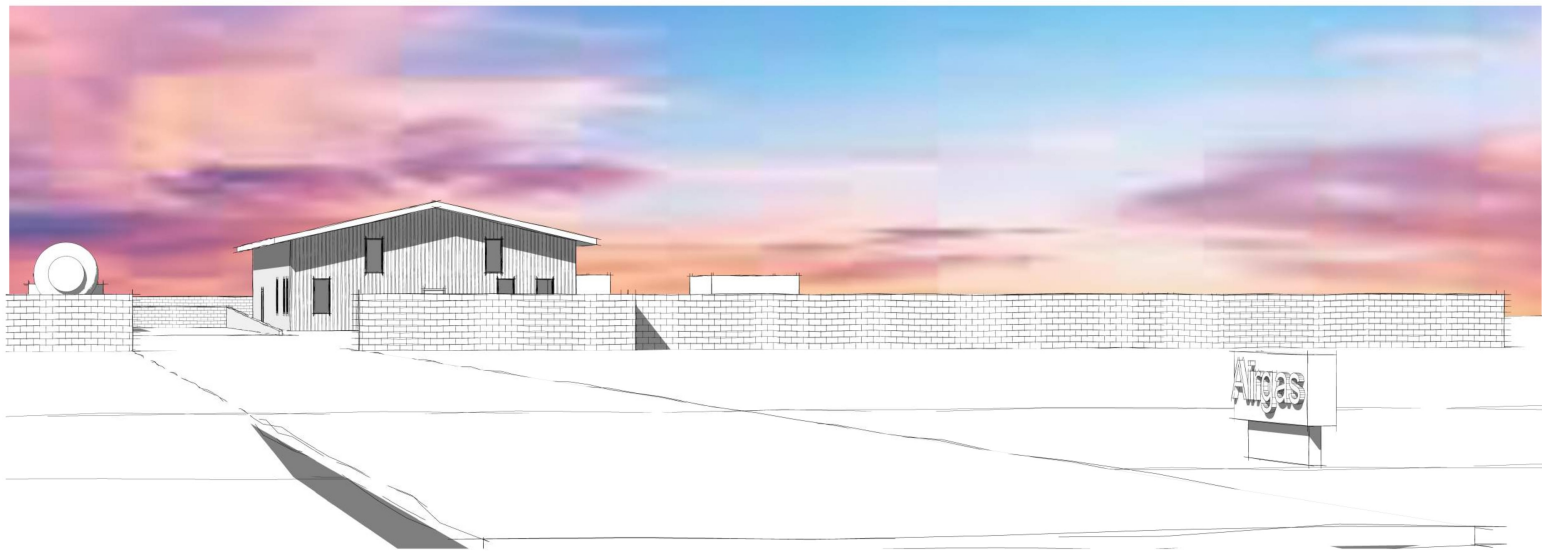


AIRGAS

PROPOSED WAREHOUSE W/ ACCESSORY OFFICES



SHEET INDEX	
SHEET NUMBER	SHEET INDEX
C1.0	COVER SHEET
C1.1	SITE IMAGES
C1.2	3D VIEWS FROM BASELINE ROAD
C1.3	3D VIEWS FROM S MILLER ROAD
C1.4	3D VIEWS FROM COLLECTOR STREET
G0.0	BUILDING CODE DATA
G1.1A	ACCESSIBILITY DETAILS
G1.1B	ACCESSIBILITY DETAILS
G1.1C	SPECIFICATIONS
G1.1D	SPECIFICATIONS
A0.0	ZONING DATA
A0.1	SITE PLAN
A1.0	FLOOR PLAN

SHEET INDEX	
SHEET NUMBER	SHEET INDEX
A1.1	FINISH PLAN
A1.01	BATHROOM DETAILS
A1.2	REFLECTED CEILING PLAN
A1.3	FF + E PLAN
A1.4	ROOF PLAN
A2.0	ELEVATIONS
A2.1	ELEVATIONS
A2.2	ELEVATIONS B&W
A2.3	ELEVATIONS B&W
A2.4	BUILDING SECTIONS
A2.5	WALL SECTIONS
A3.0	PARTITION TYPES
A4.0	SCHEDULES
A5.0	DOOR & WINDOW DETAILS
A5.1	EXTERIOR DETAILS

COB PERMITTING REVISIONS SEAL	COBCO ENGINEERING APPROVED SEAL	REVISIONS		COB PROJECT PLAN STICKER
		1	2	
AS-BUILT SEAL	DESIGN SEAL	3		
ORIGINAL PLAN DATE	LATEST REVISION DATE	COB PLAN TRACKING# ENG-25-XXXX	SUBMITTAL:	
PROJECT NUMBER	SHEET NUMBER	COB PERMIT# ENG-24-0167		

architects
LOFT
PLLC

Paul Pellicani
AIA | NCARB | LEED AP
9375 E. Shea Blvd., Suite 100
Scottsdale, AZ 85260
Phone - (480) 410-4844

www.architectsloft.com

SEAL:



Airgas

PROPOSED
WAREHOUSE
WITH
ACCESSORY
OFFICES

SW CORNER
BASELINE RD AND S
MILLER RD

REVISIONS

#	DATE	DESCRIPTION
1	12/15/2025	FILING SET
2	12/17/2025	BID SET

NOTICE: These drawings are instruments of service and are the property of the Architect, and they are available only for review and use in accordance with this Notice. The designs shown and described herein, including all technical drawings and details thereof, are proprietary and cannot be copied, duplicated or otherwise commercially exploited, in whole or part, without the expressed written permission of the Architect. All rights reserved. It is a violation of the law for any person, without acting under the direction of a licensed architect, to offer an item in any way.
Copyright © PAUL PELLICANI, P.A.

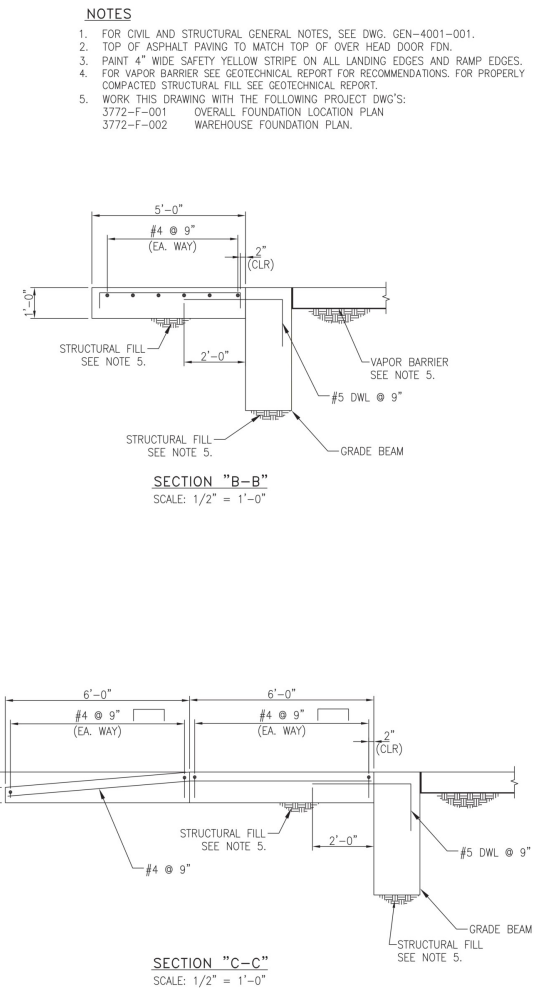
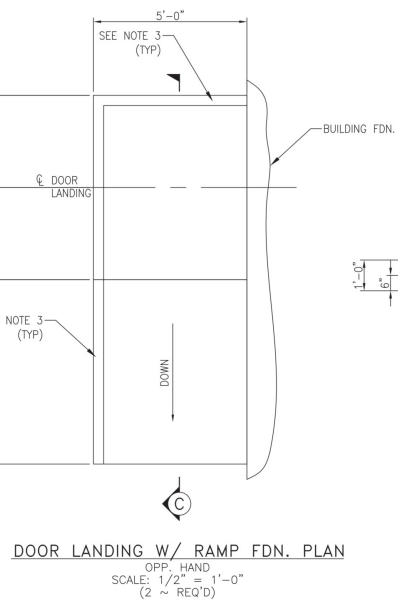
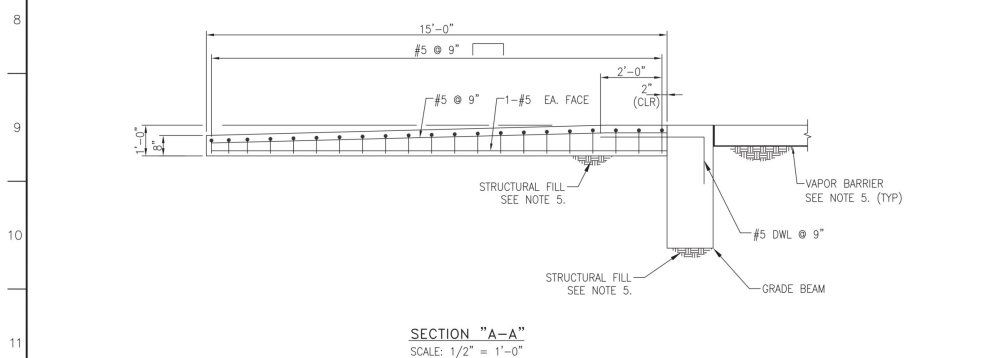
TITLE:

COVER SHEET

SCALE As Indicated
DRAWN BY Author
CHECKED BY Checker
JOB # DRAWING #
MCCOMB C1.0



Rev.



261.8 SQ FT

3772-F-005



Schembri
ENGINEERS 

www.PEInspect.com

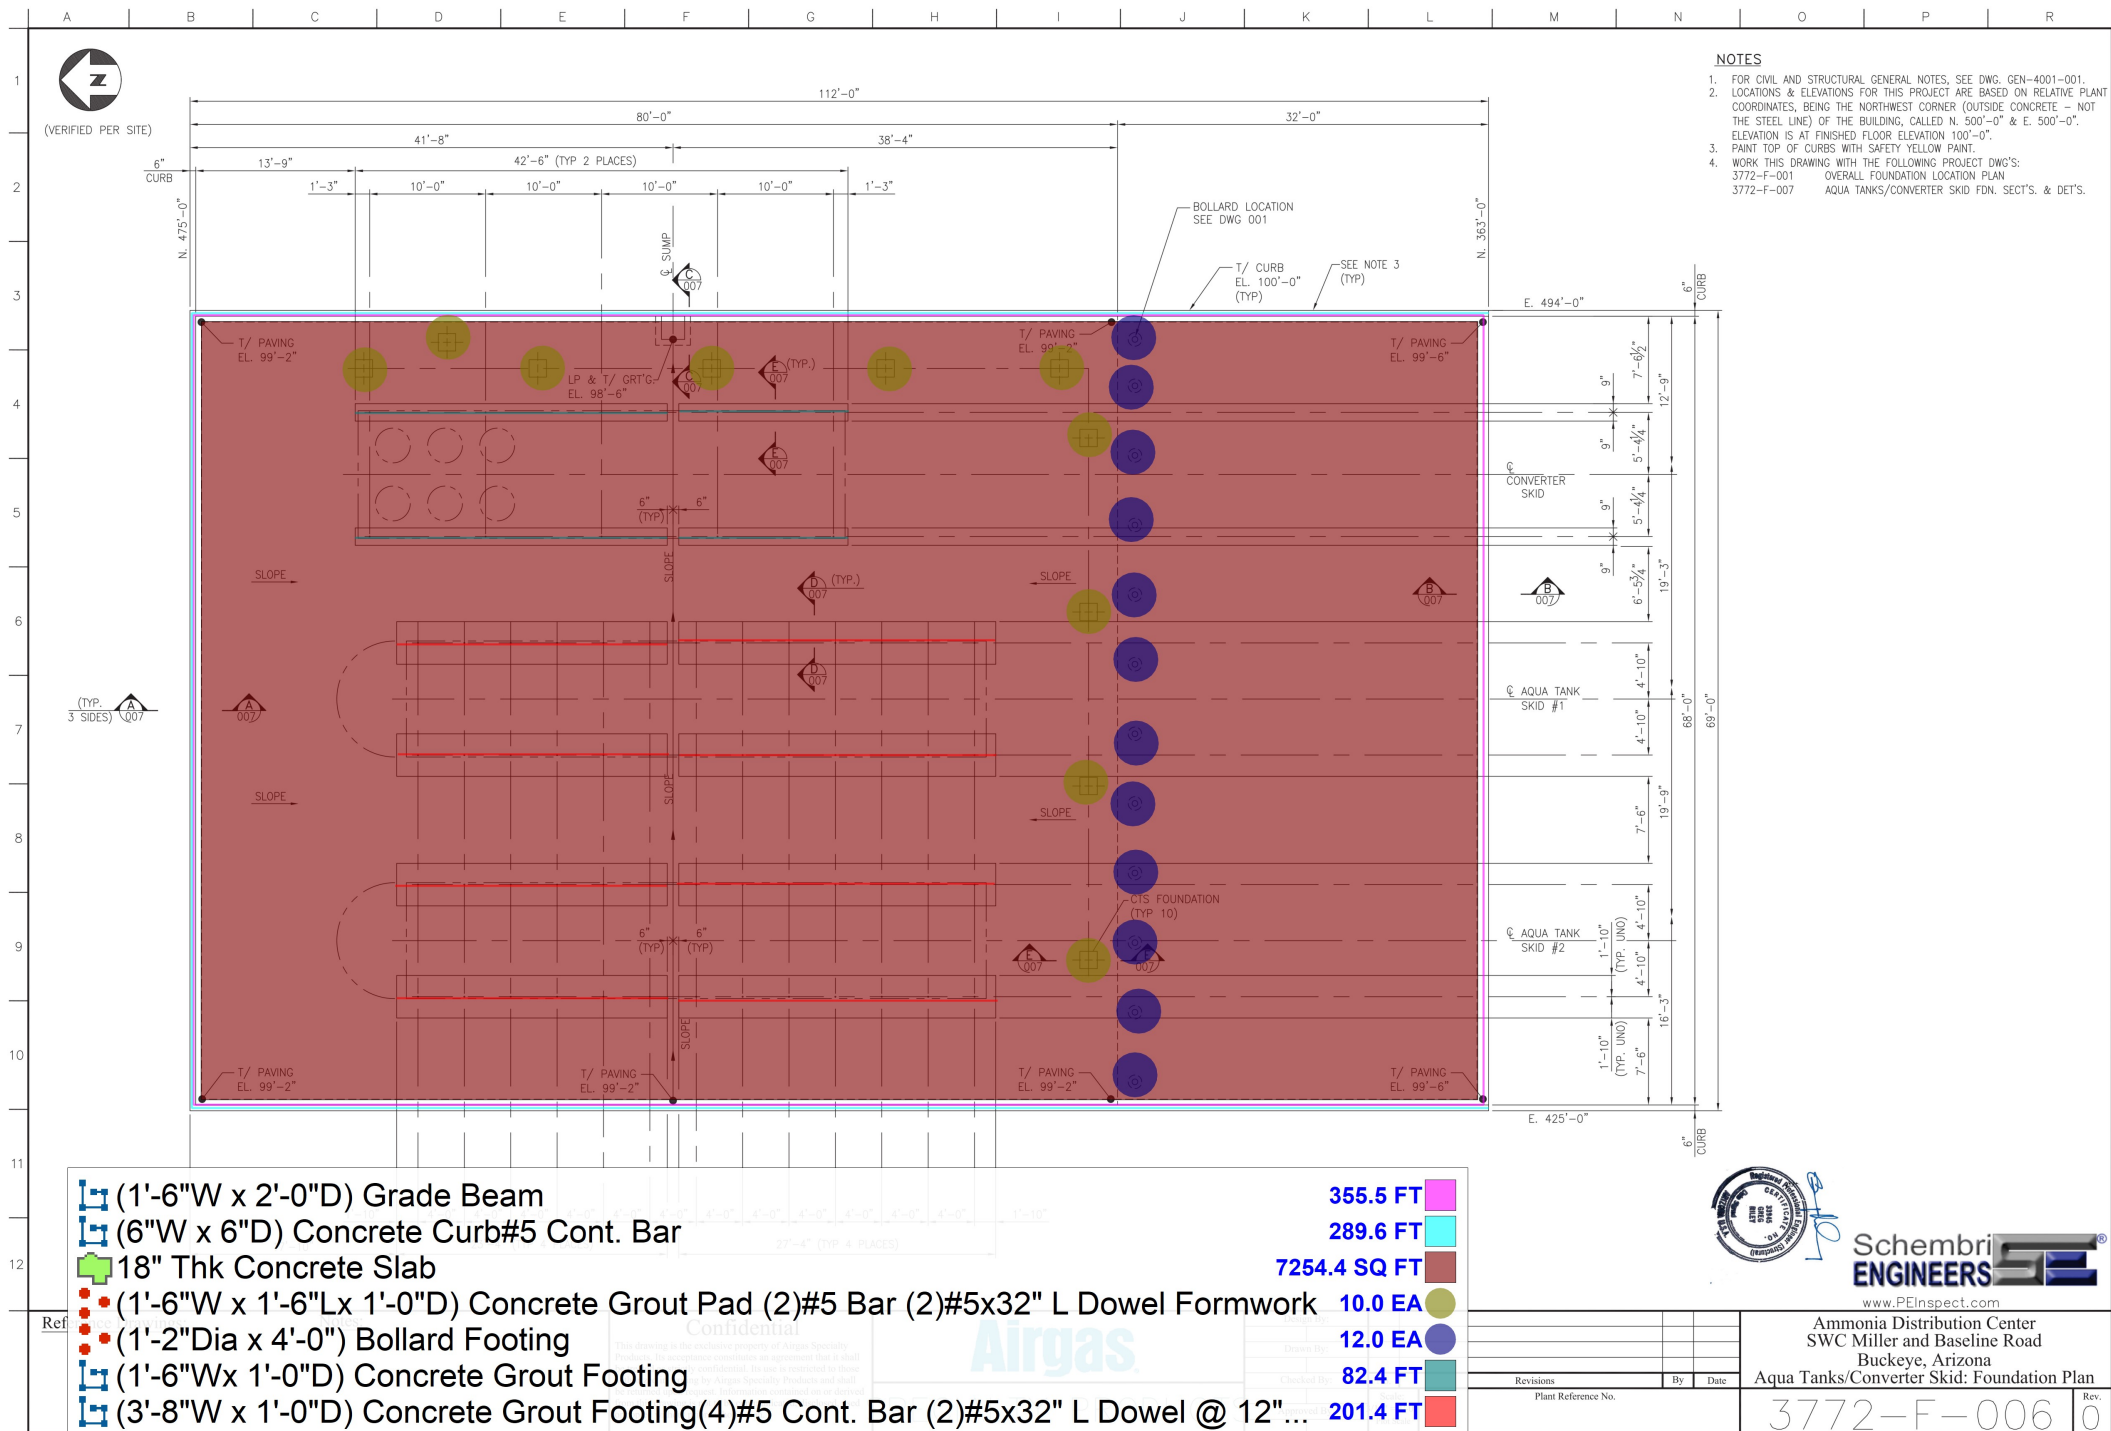
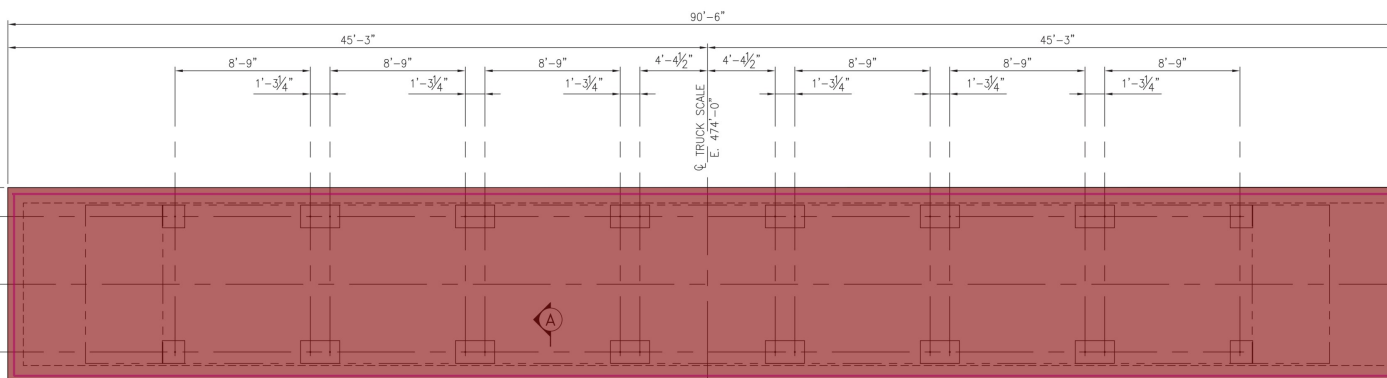


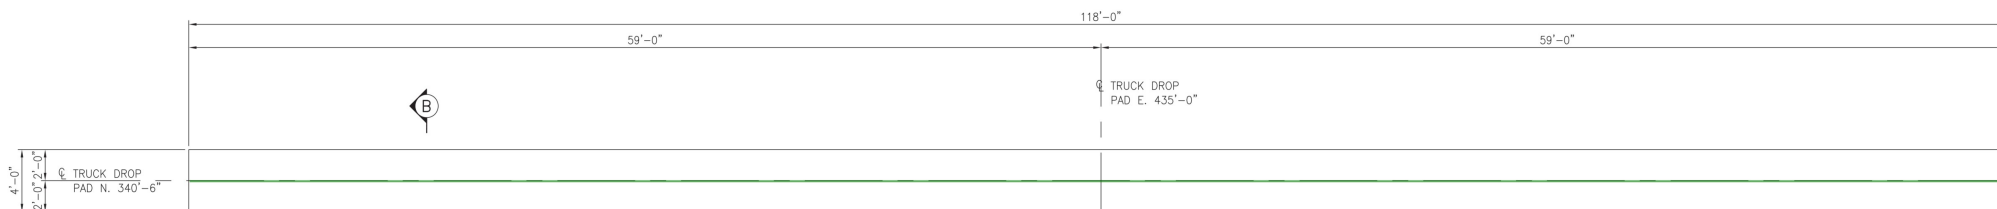


Figure 1 is a plan view of the bridge deck. The total width is 12'-6". The deck is divided into two main sections, each 6'-3" wide. Within each 6'-3" section, there is a 4'-4 9/16" wide area. The truck scale is located on the right side of the deck, with a width of 0'-0" and a label 'TRUCK SCALE' and 'N. 532'.

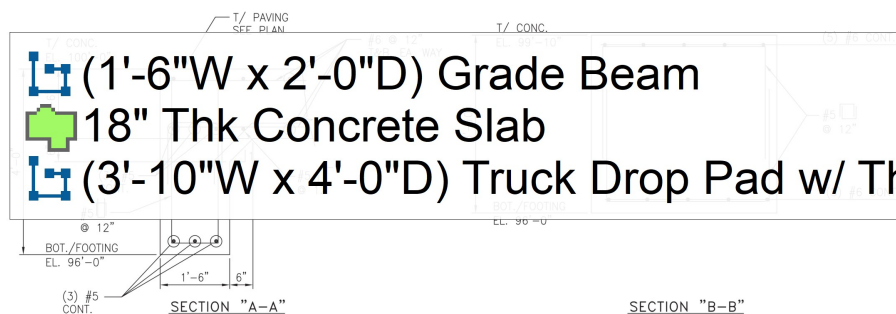


PLAN - TRUCK SCALE FOUNDATION

1. FOR CIVIL AND STRUCTURAL GENERAL NOTES, SEE DWG. GEN-4001-001.
2. LOCATIONS & ELEVATIONS FOR THIS PROJECT ARE BASED ON RELATIVE PLANT COORDINATES, BEING THE NORTHWEST CORNER (OUTSIDE CONCRETE - NOT THE STEEL LINE) OF THE BUILDING, CALLED N. 500'-0" & E. 500'-0". ELEVATION IS AT FINISHED FLOOR ELEVATION 100'-0".
3. WORK THIS DRAWING WITH THE FOLLOWING PROJECT DWGS: 3772-F-001 OVERALL FOUNDATION LOCATION PLAN



PLAN - TRUCK DROP PAD



201.3 FT
1113.2 SQ FT
117.2 FT



Schembri
ENGINEERS

www.PEInspect.com

Reference Drawings:

Notes:

Confidential

This drawing is the exclusive property of Airgas Specialty Products. Its acceptance constitutes an agreement that it shall be treated as strictly confidential. Its use is restricted to those authorized in writing by Airgas Specialty Products and shall be returned upon request. Information contained on or derived from this drawing is not to be communicated, disclosed, used or copied without prior authorization.

Airgas

SPECIALTY PRODUCTS

Design By:

Drawn By:

Checked By:

Approved By _____

	Yes	No
--	-----	----

Re

Se

Plant Reference No. _____

Ammonia Distribution Center
SWC Miller and Baseline Road
TRUCK SCALE & TRUCK DROP PAD
Truck Scale and Drop-Off Pad: Foundation Plan

3772-F-009

	Re
	C