ADD / ALTER B210 COMMUNICATIONS

173RD CIVIL ENGINEERING SQUADRON

KINGSLEY FIELD ANG BASE, OREGON

PROJECT NUMBER: KJAQ199077

SEPTEMBER 2024

TYPE B-3 FINAL

REGISTERED PROFESSIONAL ENGINEER
83025PE
OREGON
JANUARY 08, 2008
DENNIS R. PEARSON
EXPIRES: DEC 31, 2026

NO.	DATE	BY	REVISION	CHK	APVD
DSGN	J. ANDERSON	DR	J. ANDERSON	E. HANBICKI	D. PEARSON

© JACOBS 2023. ALL RIGHTS RESERVED.

1100 NE CIRCLE BOULEVARD, SUITE 300
CORVALLIS, OREGON 97330

ADD/ALTER B210 COMMUNICATIONS
ANG PROJECT NO. KJAQ199077
OREGON AIR NATIONAL GUARD
KINGSLEY FIELD ANG BASE, OR

GENERAL
COVER SHEET

VERIFY SCALE
BAR IS ONE INCH ON ORIGINAL DRAWING.
0 1"

DATE SEPTEMBER 2024
PROJ FA877010
DWG G-001

TYPE B-3 FINAL

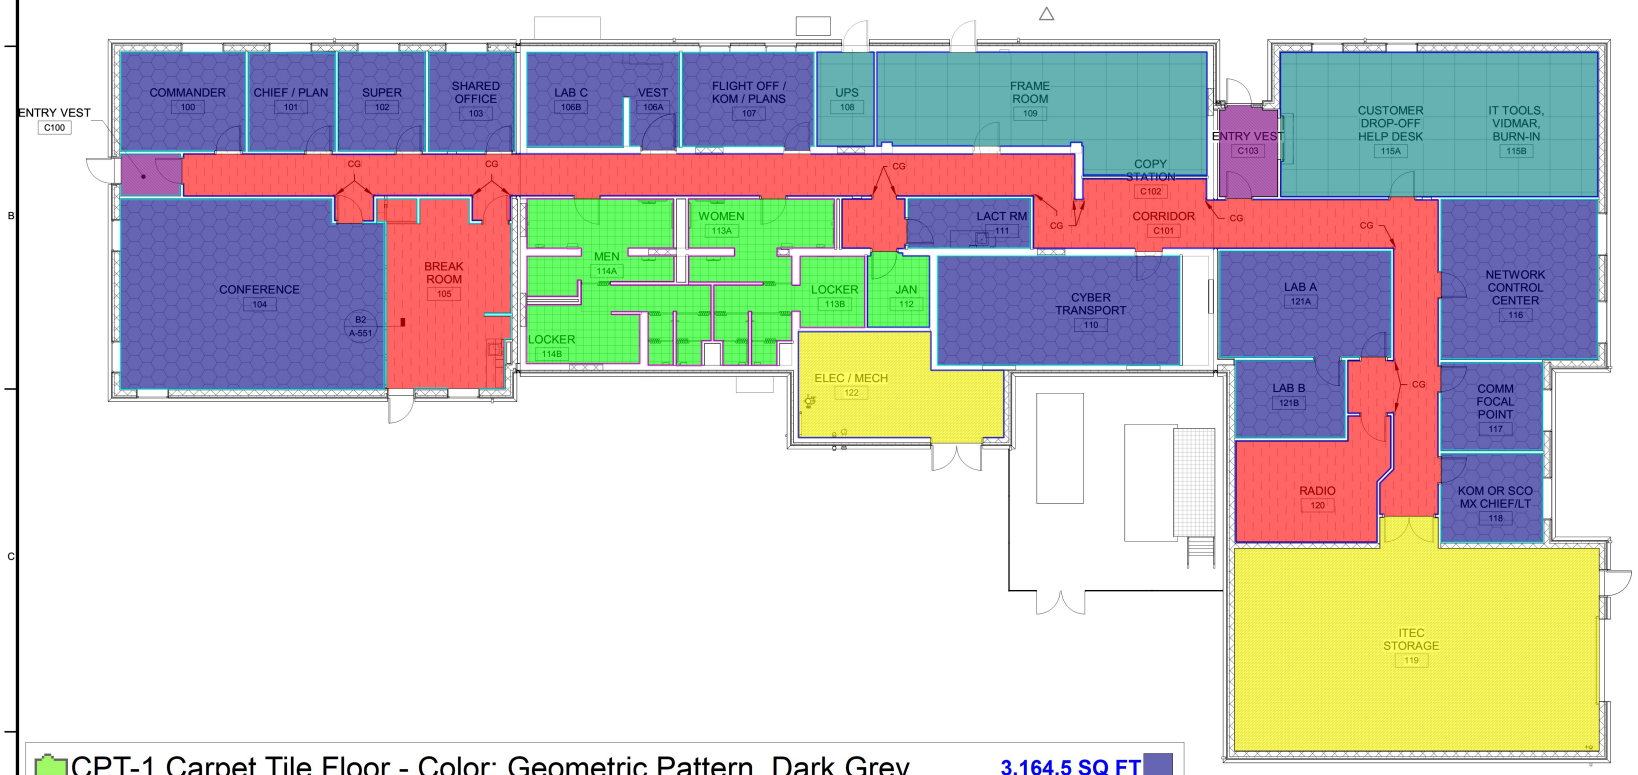

CPT-1 Carpet Tile Floor - Color: Geometric Pattern, Dark Grey	3,164.5 SQ FT
CPT-2 Broadloom Heavy-Duty Entrance Carpet Floor - Color: Black	114.2 SQ FT
SDT-1 Static Dissipative Vinyl Floor - Color: Light Grey	1,260.7 SQ FT
LVT-1 Luxury Vinyl Tile Floor - Color: Light Grey	1,737.7 SQ FT
PMT-1 (3"x3")Porcelain Mosaic Tile Floor - Color: Grey	729.2 SQ FT
S/H-1 Sealer/Hardener Concrete Floor - Color: Clear	1,392.2 SQ FT
RB-1 4" Resilient Base - Cove - Color: Black	767.6 FT
PCT-1 (6"x12") Porcelain Tile - Cove Base - Color: Grey	310.4 FT
RB-2 4" Resilient Base - Straight - Color: Black	879.6 FT

GENERAL NOTES

LEGEND

CPT-1 EPX-1 PMT-1 SDT-1
CPT-2 LVT-1 S/H-1

CG INDICATES 2 1/2" LEG, 48" LONG STAINLESS STEEL CORNER GUARD

KEYPLAN

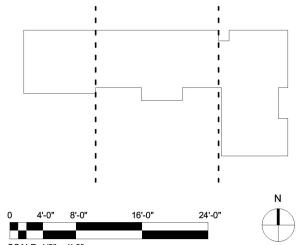

SCALE: 1/8" = 1'-0"

REGISTERED ARCHITECT
JULIAN ANDERSON
BELLEVUE, WA
LIC # ARI-14706
STATE OF OREGON

© JACOBS 2023. ALL RIGHTS RESERVED.

NO.	DATE	DSGN	DR	CHK	REVISION	APVD	BY
		J. ANDERSON	J. ANDERSON	E. HANBICKI		APVD	D. PEARSON

1100 NE CIRCLE BOULEVARD, SUITE 300
CORVALLIS, OREGON 97330

Jacobs

INTERIORS

ADD/ALTER B210 COMMUNICATIONS
ANG PROJECT NO. KJAQ199077
OREGON AIR NATIONAL GUARD
KINGSLEY FIELD ANG BASE, OR

FINISH FLOOR PLAN

1/8" = 1'-0"
VERIFY SCALE
BAR IS ONE INCH ON ORIGINAL DRAWING.
0 1"

DATE SEPTEMBER 2024
PROJ FA877010
DWG I-101

TYPE B-3 FINAL