

STERLING GENERAL INVESTMENTS, LLC

Lewisville Restaurant

New Construction

2000 FM 544, Lewisville, TX 75056



BB+W
ARCHITECTS

24080 Hwy 59 North, Ste. 150 Phone: 281-901-0331
Kingwood, TX 77339 Contact@BBWArchitects.com

SEALS:



DATE: 12/01/2025

CONSULTANT:

Lewisville
Restaurant

2000 FM 544, Lewisville,
TX 75056

New Construction

NOTE:
These drawings may have been reproduced at a size
different than originally drawn. Owner and
architect assume no responsibility for use of
incorrect scale.

Contractor shall verify all existing conditions prior
to proceeding with construction. Notify BB&W
Architects, LLC immediately of any discrepancies
or conflicts. All dimensions to face of finish, UNO.

Date	Nr.	Description
11/20/2025		Issue for Permit & Pricing

PROJECT NR.: 25005
ISSUE DATE: 12/01/2025
PRINT DATE: 12/01/2025
CLIENT: STERLING GENERAL
INVESTMENTS, LLC

COPYRIGHT:
BB&W Architects, LLC expressly reserves its
common law copyright and other property rights in
these drawings. They are not to be reproduced,
changed, or copied in any form or manner
whatsoever, nor are they to be assigned to any third
party without first obtaining the expressed written
permission and consent of the firm.

SHEET TITLE:
TITLESHEET

ARCHITECT
BB&W Architects, LLC
24080 Hwy 59 North, Suite 150
Kingwood, TX 77339
(281) 901-03331

LANDSCAPE ARCHITECT
Land Design
5217 Alpha Road, Suite 140
Dallas, TX 75240
(214) 785-6009


CIVIL ENGINEER
Land Design
5217 Alpha Road, Suite 140
Dallas, TX 75240
(214) 785-6009

STRUCTURAL ENGINEER
ASI Construction & Consulting, LLC
P.O. Box 1391
League City, TX 77573
(281) 819-0121

MEP
SPECTRUM Design Engineers
19 Sierra Oaks Drive
Sugar Land, TX 77479
(832) 766-6076

KITCHEN CONSULTANT
Five Oaks Kitchen Design
10206 Five Oaks Lane
Missouri City, TX 77459
(713) 705-0952, Fax (281) 778-8536
info@fiveoakskitchendesign.com

G000

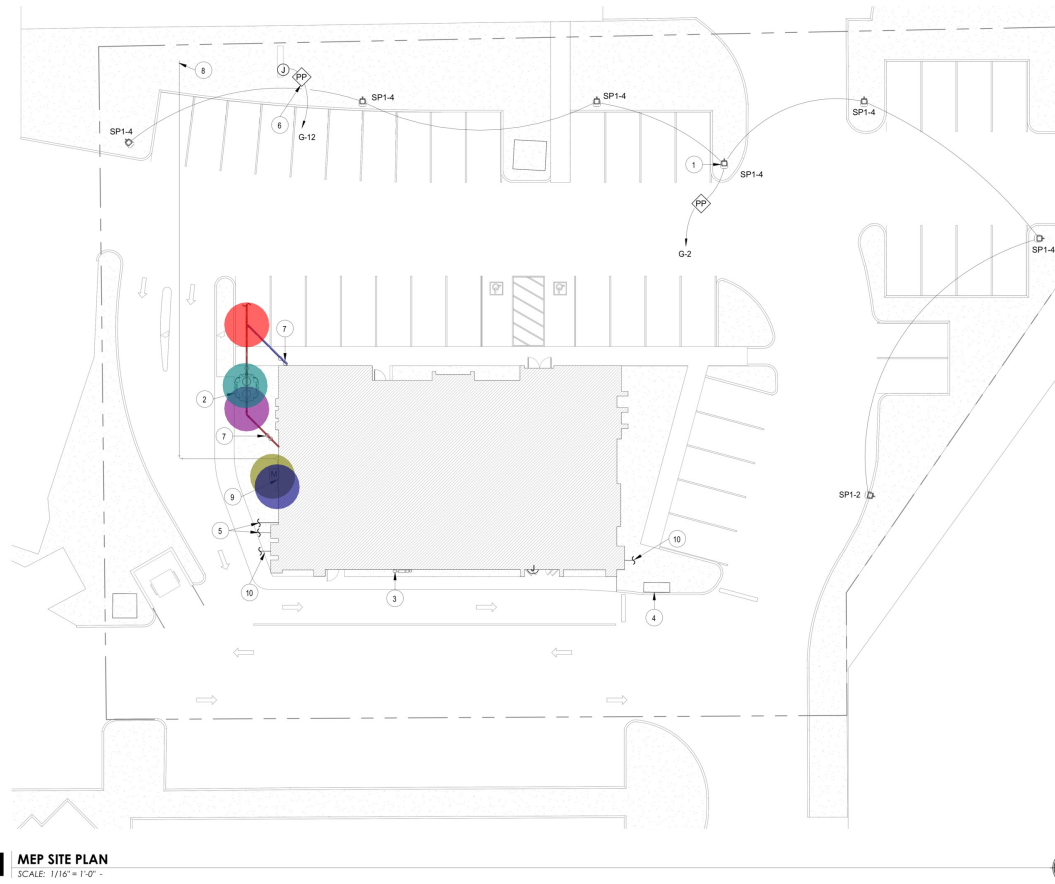

1 MEP SITE PLAN
SCALE: 1/16" = 1'-0"

- Natural Gas Utility Meter
- Gas Utility Regulator Gas Cock
- (4" Dia) Grease Waste Pipe
- (4" Dia) Sanitary Waste Pipe
- (4"x4"x4") Wye
- (4" Dia) 45 Degree Elbow
- Grease Trap

- 1.0 EA
- 1.0 EA
- 40.0 FT
- 14.4 FT
- 1.0 EA
- 1.0 EA
- 1.0 EA

KEYED NOTES

1. PROVIDE POWER TO EXTERIOR LIGHTING THROUGH CIRCUIT INDICATED. REFER TO ARCHITECTURAL PLANS FOR EXACT LOCATIONS OF LIGHT FIXTURES. PROVIDE TIMECLOCK/PHOTOCELL CONTROL OF LIGHTS PER 2021 IECC THROUGH WIRELESS HUB. POWER PACK SHOWN SHALL BE INSTALLED INDOORS NEAR WIRELESS HUB.
2. PROVIDE BELOW GRADE GREASE TRAP EQUIVALENT TO SCHER QB-1000 WITH SAMPLE WELL EQUIVALENT TO SCHER DV-10. SEE DETAIL. COORDINATE EXACT LOCATION WITH CIVIL ENGINEER AND OWNER.
3. ELECTRICAL UTILITY CT CABINET AND METER. PROVIDE SERVICE ENTRANCE RATED DISCONNECT AND GUTTER PER ONE-LINE. RE: ELECTRICAL ONE-LINE DIAGRAM.
4. EXISTING PAD MOUNTED ELECTRICAL UTILITY TRANSFORMER. VERIFY WITH UTILITY THIS TRANSFORMER SHALL SERVE BUILDING. SEE CIVIL PLAN FOR EXACT LOCATION. RE: ELECTRICAL ONE-LINE DIAGRAM.
5. 2" CW AND 6" FIRE WATER FROM UTILITY. REFER TO CIVIL FOR CONTINUATION.
6. PROVIDE POWER TO MONUMENT SIGNAGE THRU LOCAL DISCONNECT MEANS. COORDINATE INSTALLATION WITH SIGNAGE VENDOR. PROVIDE CONTROL OF SIGNAGE THROUGH WIRELESS HUB FOR PHOTOCELL/TIMECLOCK TO MEET 2021 IECC. INSTALL POWER PACK INSIDE BUILDING.
7. PROVIDE TWO-WAY CLEANOUT PER DETAIL AT EXTERIOR OF BUILDING.
8. ASSUMED LOCATION OF CONNECTION POINT TO UTILITY GAS MAIN. COORDINATE WITH NATURAL GAS UTILITY PROVIDER TO ROUTE NATURAL GAS TO BUILDING. COORDINATE EXACT ROUTING WITH CIVIL ENGINEER.
9. NATURAL GAS UTILITY REGULATOR, METER, AND GAS COCK FOR CONNECTED GAS LOAD OF 2,061 CFH. COORDINATE REQUIREMENTS WITH UTILITIES TERMS AND CONDITIONS PACKAGE.
10. 8" PRIMARY BELOW GRADE STORM PIPING. SEE CIVIL PLAN FOR CONTINUATION.

SEALS:



DATE:

CONSULTANT:



Lewisville Restaurant

2000 FM 544, Lewisville,
TX 75056

New Construction

NOTE:

These drawings may have been reproduced at a size different than originally drawn. Owner and architect assume no responsibility for use of incorrect scale.

Contractor shall verify all existing conditions prior to proceeding with construction. Notify BB+W Architects, LLC immediately of any discrepancies or conflicts. All dimensions to face of finish, U.N.C.

Date	Nr.	Description

PROJECT NR.: 25005

ISSUE DATE: Issue Date

PRINT DATE:

CLIENT: STERLING GENERAL INVESTMENTS, LLC


COPYRIGHT:

BB+W Architects, LLC expressly reserves its common law copyright and other property rights in these drawings. They are not to be reproduced, changed, or copied in any form or manner whatsoever, nor are they to be assigned to any third party without first obtaining the expressed written permission and consent of the firm.

SHEET TITLE:

MEP SITE PLAN

MEP1.01

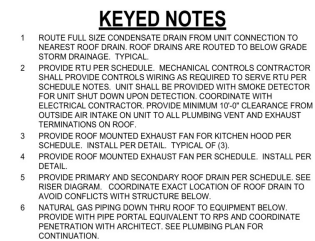

24080 Hwy 59 North, Ste. 150
Kingwood, TX 77339

Phone: 281-901-0331
Contact@BBWArchitects.com

SEALS:



DATE: _____

CONSULTANT:



Louisville
Restaurant

2000 FM 544, Lewisville,
TX 75056

New Construction

NOTE:

Contractor shall verify all existing conditions prior to proceeding with construction. Notify **BB&W Architects, LLC** immediately of any discrepancies or conflicts. All dimensions to face of finish, U.N.O.

[illegible]

PROJECT NR.: 25005

ISSUE DATE: Issue Date

PRINT DATE:

CLIENT: STERLING

INVESTMENTS, LLC

COPYRIGHT:

BB&W Architects, LLC expressly reserves its common law copyright and other property rights in these drawings. They are not to be reproduced, changed, or copied in any form or manner whatsoever, nor are they to be assigned to any third party without first obtaining the expressed written permission and consent of the firm.

SHEET TITLE:

MEP ROOF PLAN

MEP1.02

- RTU-1
- RTU-2
- MAU-D1
- MAU-A9
- EF-1
- EF-2
- EF-3
- EF-4
- (1 1/4" Dia) Natural Gas Pipe
- (2 1/2" Dia) Natural Gas Pipe
- (1" Dia) Natural Gas Pipe
- (3" Dia) Natural Gas Pipe
- (3" Dia) 90 Degree Elbow
- (1 1/4" Dia) 90 Degree Elbow
- (1" Dia) 90 Degree Elbow
- (3"x1 1/4"x3") Tee
- (3"x1"x3") Tee
- (3"x1"x2 1/2") Tee
- (2 1/2"x1 1/2"x2 1/2") Tee
- (3"x1"x3") Tee

- 1.0 EA 
1.0 EA 
1.0 EA 
1.0 EA 
1.0 EA 
1.0 EA 
1.0 EA 
1.0 EA 
51.6 FT 
9.6 FT 
21.4 FT 
31.5 FT 
1.0 EA 
2.0 EA 
2.0 EA 
1.0 EA 
1.0 EA 
1.0 EA 
1.0 EA 
1.0 EA 

SEALS:



DATE:

CONSULTANT:



**Lewisville
Restaurant**

2000 FM 544, Lewisville,
TX 75056

New Construction

NOTE:

These drawings may have been reproduced at a size different than originally drawn. Owner and architect assume no responsibility for use of incorrect scale.
Contractor shall verify all existing conditions prior to proceeding with construction. Notify BB+W Architects, LLC immediately of any discrepancies or conflicts. All dimensions to face of finish, U.N.C.

Date	Nr.	Description

PROJECT NR.: 25005

ISSUE DATE: Issue Date

PRINT DATE:

CLIENT: STERLING GENERAL INVESTMENTS, LLC

COPYRIGHT:

BB+W Architects, LLC expressly reserves its common law copyright and other property rights in these drawings. They are not to be reproduced, changed, or copied in any form or manner whatsoever, nor are they to be assigned to any third party without first obtaining the expressed written permission and consent of the firm.

SHEET TITLE:


PLUMBING RISER
DIAGRAM

P4.01

2 PLUMBING RISER DIAGRAM - WATER

SCALE: -

(1/2" Dia) Cold Water Pipe	315.1 FT
(1 1/2" Dia) Cold Water Pipe	23.0 FT
(1/2" Dia) Hot Water Pipe	195.3 FT
(3/4" Dia) Cold Water Pipe	41.0 FT
(3/4" Dia) Hot Water Pipe	30.0 FT
(1 1/4" Dia) Hot Water Pipe	8.1 FT
(1 1/4" Dia) Cold Water Pipe	7.3 FT
(2" Dia) Cold Water Pipe	18.1 FT
(6" Dia) Fire Water Service Pipe	18.2 FT
(2" Dia) Vent Pipe	294.0 FT
(3" Dia) Vent Pipe	33.7 FT
(2" Dia) Sanitary Waste Pipe	41.1 FT
(4" Dia) Sanitary Waste Pipe	15.9 FT
(3" Dia) Sanitary Waste Pipe	30.3 FT
(3" Dia) Grease Waste Pipe	56.8 FT
(4" Dia) Grease Waste Pipe	16.4 FT

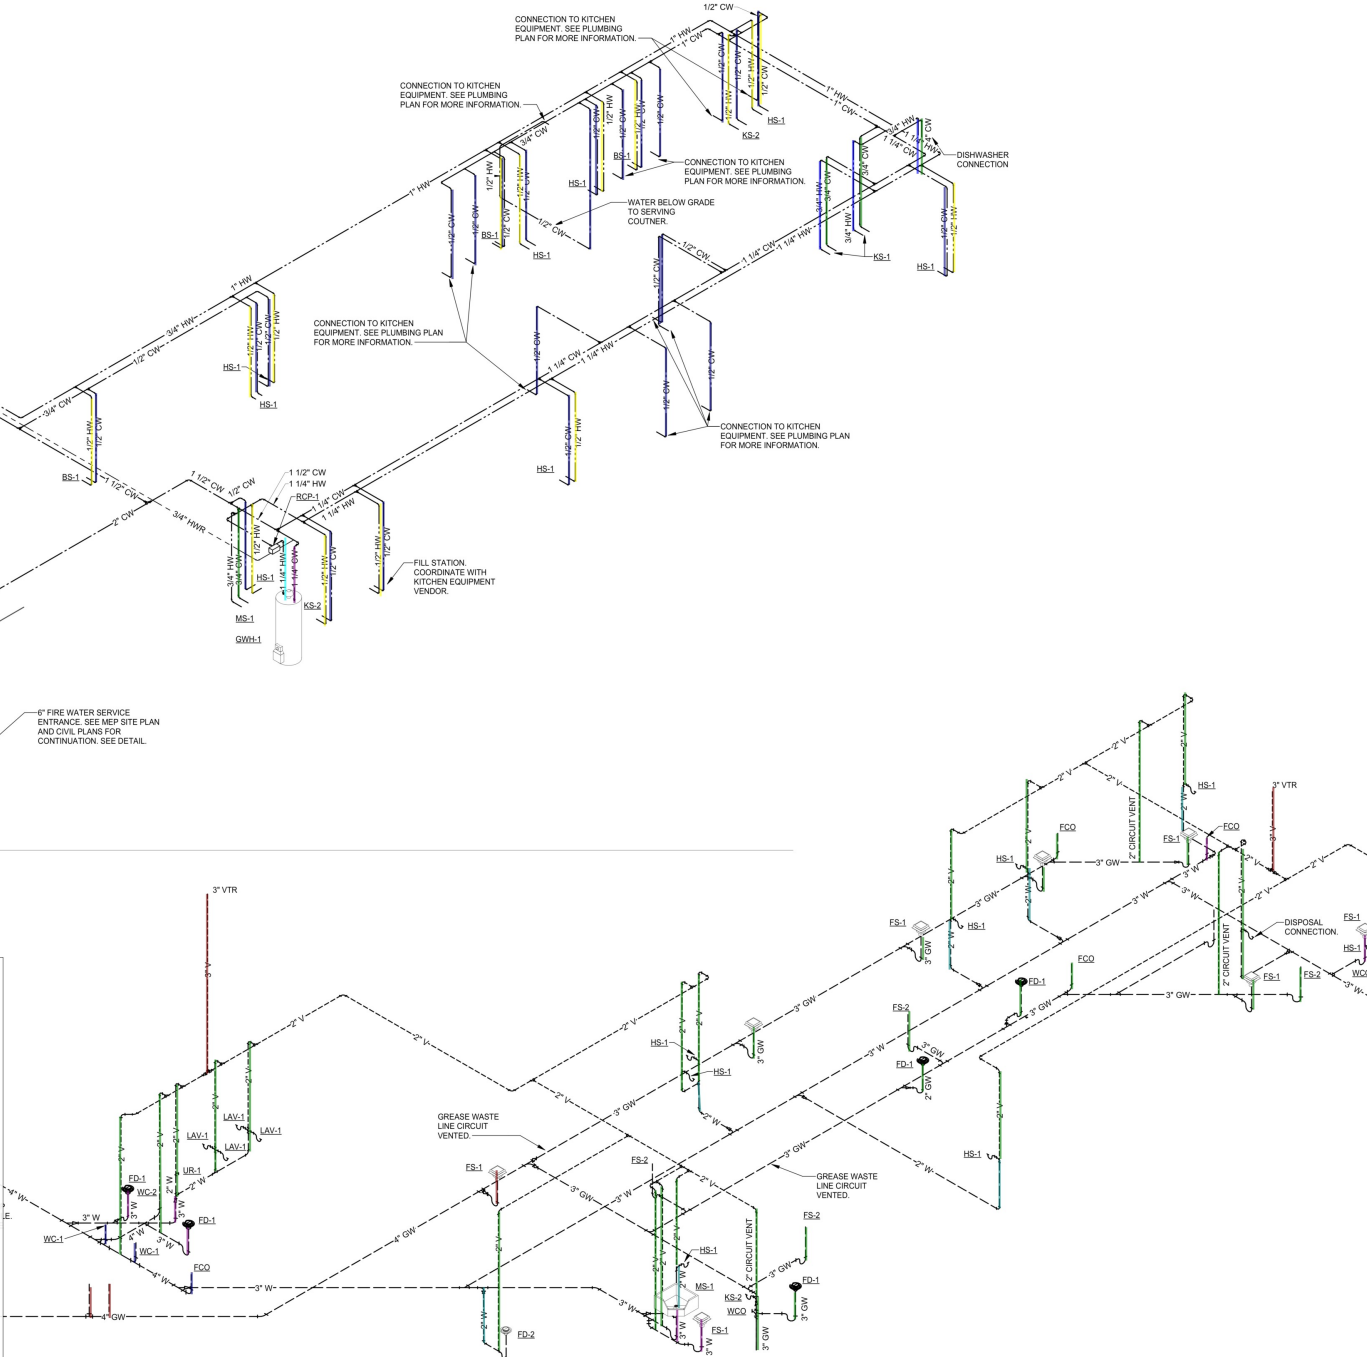

SEALS:



DATE:

CONSULTANT:



Lewisville Restaurant

2000 FM 544, Lewisville,
TX 75056

New Construction

NOTE:

These drawings may have been reproduced at a size different than originally drawn. Owner and architect assume no responsibility for use of incorrect scale.

Contractor shall verify all existing conditions prior to proceeding with construction. Notify BBW Architects, LLC immediately of any discrepancies or conflicts. All dimensions to face of finish, U.N.C.

Date	Nr.	Description

PROJECT NR.: 25005

ISSUE DATE: Issue Date

PRINT DATE:

CLIENT: STERLING GENERAL INVESTMENTS, LLC


COPYRIGHT:

BBW Architects, LLC expressly reserves its common law copyright and other property rights in these drawings. They are not to be reproduced, changed, or copied in any form or manner whatsoever, nor are they to be assigned to any third party without first obtaining the expressed written permission and consent of the firm.

SHEET TITLE:

PLUMBING RISER
DIAGRAM

P4.02

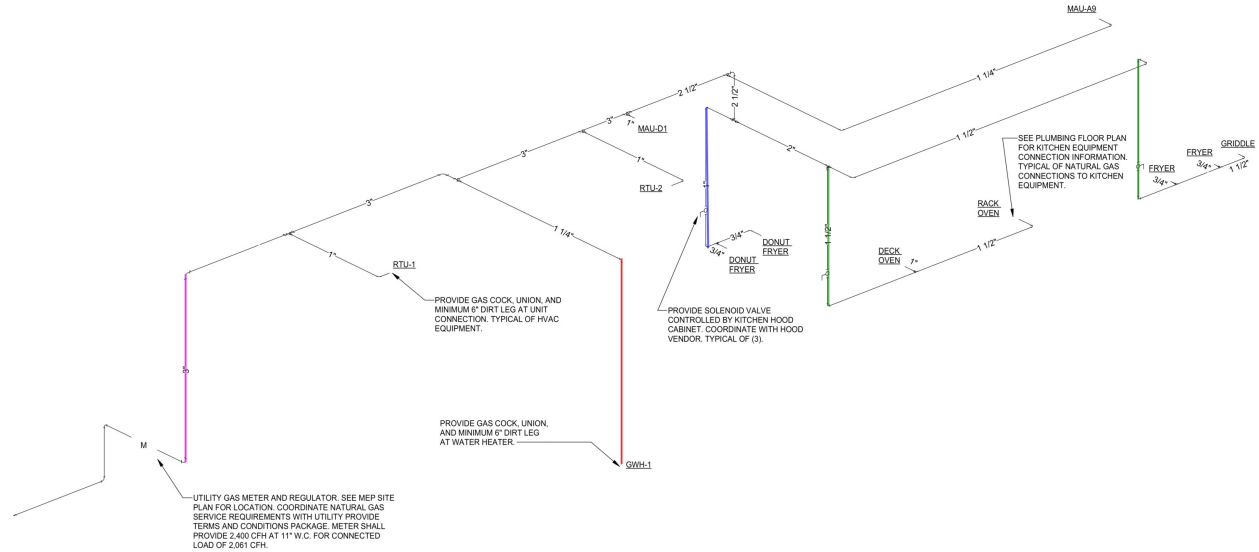

1 PLUMBING RISER DIAGRAM - NATURAL GAS
SCALE: -

- (3" Dia) Natural Gas Pipe
- (1" Dia) Natural Gas Pipe
- (1 1/4" Dia) Natural Gas Pipe
- (1 1/2" Dia) Natural Gas Pipe
- (5" Dia) Storm Drain Pipe


24.2 FT

18.0 FT

26.4 FT

35.9 FT

106.8 FT

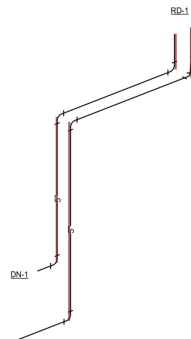

2 PLUMBING RISER DIAGRAM - STORM DRAINAGE
SCALE: -

