


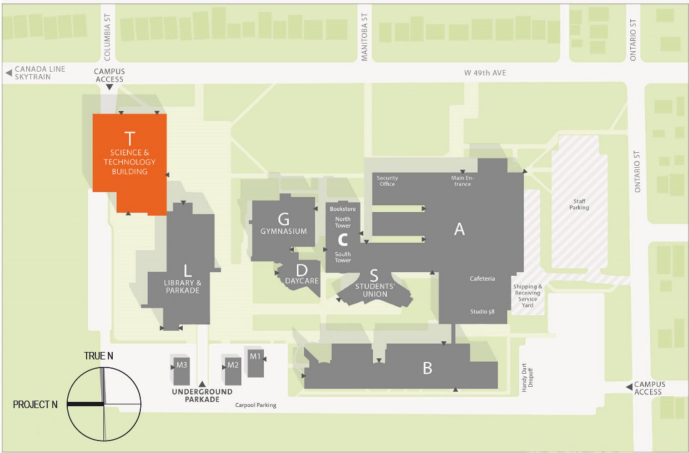

CAMPUS PLAN

ARCHITECTURAL DRAWING LIST

DWG.	DRAWING NAME
A-000	COVER PAGE
A-002	EXISTING PHOTOS
A-020	3D BUILDING IMAGES
A-021	RENDERINGS
A-025	GENERAL NOTES
A-030	CONTEXT PLAN
A-040	CODE REVIEW & CODE PLANS - LEVEL 3
A-050	DOOR SCHEDULE & FRAME PROFILE & PANEL TYPES
A-081	INTERIOR WALL & CEILING TYPES
A-100	PROJECT SCOPE PLANS
A-110	LEVEL 3 EXISTING & DEMOLITION PLAN
A-200	LEVEL 3 OVERALL FLOOR PLAN
A-201	LEVEL 3 WALL PROTECTION DIAGRAM
A-210	LEVEL 3 DEMO REFLECTED CEILING PLAN
A-250	OVERALL REFLECTED CEILING PLANS
A-400	WALL SECTIONS
A-580	PLAN DETAILS
A-590	SECTION DETAILS
A-591	SECTION DETAILS
A-600	ENLARGED FLOOR PLAN - NURSING LAB & OFFICE
A-601	ENLARGED FLOOR PLANS - SIM SUITES, WORK ROOM & PRACTICE LAB
A-650	INTERIOR ELEVATIONS - NURSING LAB
A-651	INTERIOR ELEVATIONS - NURSING LAB
A-652	INTERIOR ELEVATIONS - NURSING LAB
A-653	INTERIOR ELEVATIONS - NURSING LAB
A-654	INTERIOR ELEVATIONS - NURSING LAB
A-655	INTERIOR ELEVATIONS - OFFICE
A-656	INTERIOR ELEVATIONS - PRACTICE LAB
A-657	INTERIOR ELEVATIONS - PRACTICE LAB
A-658	INTERIOR ELEVATIONS - TYP. SIM SUITE
A-659	INTERIOR ELEVATIONS - WORKROOM

PROJECT STATISTICS

CIVIC ADDRESS:
170 W 49TH AVENUE, VANCOUVER, BC V5Y 2Z6

LEGAL DESCRIPTION:
PLAN VAP12842 DISTRICT LOT 526 NWD GROUP 1.

ZONING:
CD-1 (55)

OCCUPANCY & USE:
GROUP A, DIVISION 2 (CLASSROOMS, LABS & WORKSHOPS)

AREAS:
Site Area - 57,647m²
Building Gross Floor Area - 13,190m²
Building Net FSR Area - 11,766
Scope of Work Area -
Level 3: 675m²

SCOPE OF WORK:
Level 3: The minor renovation of three existing physics labs, being converted to a nursing lab, office, prep/work room and a suite of six simulation labs.



LANGARA NURSING EXPANSION RENOVATION

170 W 49TH AVE, VANCOUVER BC

25-09




ISSUED FOR TENDER
DECEMBER 5, 2025

STRUCTURAL	MECHANICAL	ELECTRICAL
WSB ENGINEERING 3855 HENNING DR #115 BURNABY, BC V5C 6N3	AME GROUP 205-635 SMITH ST VANCOUVER, BC V6B 1E3	AES ENGINEERING 300-151 EAST 2ND AVE VANCOUVER, BC V5T 1B4

-  SF1 Wall (2780mm H)
-  SF4 Wall (2780mm H)
-  S4a Wall (2780mm H)
-  S6 Wall (2780mm H)
-  S6a Wall (2780mm H)
-  S4D Wall (2780mm H)
-  S4Da Wall (2780mm H)

-  11.4 M
-  34.7 M
-  2.8 M
-  4.7 M
-  22.5 M
-  1.1 M
-  1.1 M

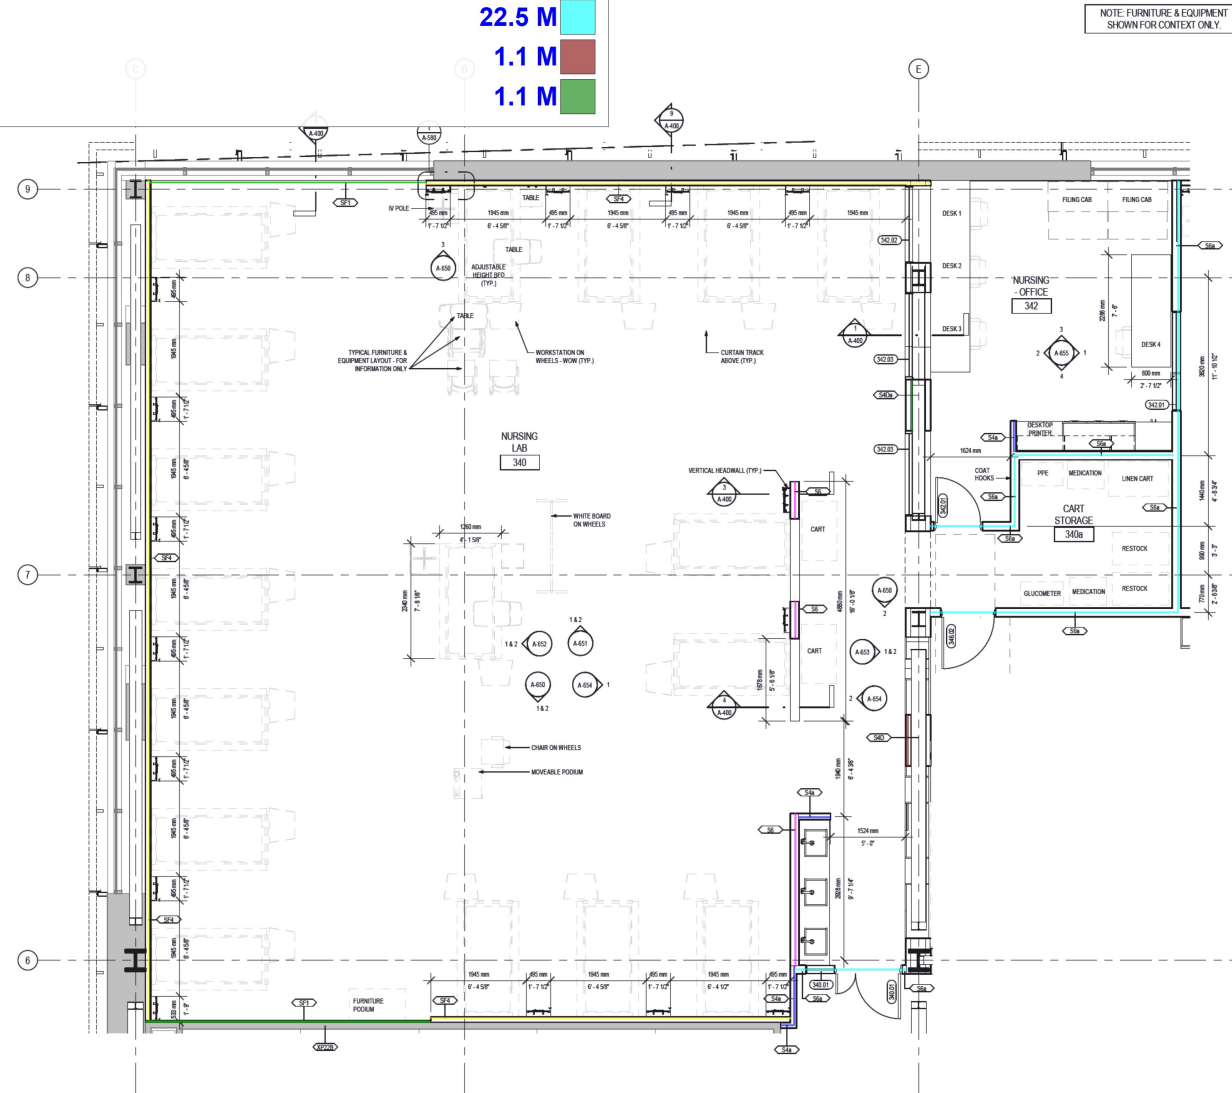

1 ENLARGED PLAN - LEVEL 3 - NURSING LAB & OFFICE
1 : 50

PROSCENIUM ARCHITECTURE + INTERIORS INC.

300-101 EAST 2ND AVE
VANCOUVER BC V6T 1B4 CANADA
604.679.0708
www.proscenium.ca

ALL OF THE DOCUMENTS PREPARED BY PROSCENIUM ARCHITECTURE + INTERIORS INC. OR ON BEHALF OF PROSCENIUM ARCHITECTURE + INTERIORS INC. IN CONNECTION WITH THE PROJECT ARE INSTRUMENTS OF SERVICE FOR THE EXECUTION OF THE PROJECT. PROSCENIUM ARCHITECTURE + INTERIORS INC. RESERVES THE RIGHT TO MAKE ANY CHANGES TO THESE DOCUMENTS WITHOUT NOTICE. THESE DOCUMENTS MAY NOT BE USED FOR ANY OTHER PROJECT WITHOUT PRIOR WRITTEN AGREEMENT OF PROSCENIUM ARCHITECTURE + INTERIORS INC. DO NOT SCALE DRAWINGS.


(for Building Official's Use)

(for Certified Professional's Use)

KEY PLAN

ISSUED FOR TENDER 2025.12.05
ISSUED FOR BUILDING PERMIT 2025.09.17
ISSUED FOR BP DRAFT 2025.08.28

NO.	DESCRIPTION	BY	DATE
1	CURRENT REVISION		

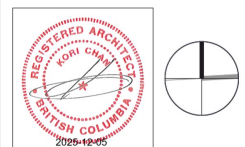


PROJECT ADDRESS
170 W 49TH AVE, VANCOUVER BC

PROJECT
LANGARA NURSING EXPANSION RENOVATION

DRAWING TITLE	PROJECT NUMBER
ENLARGED FLOOR PLAN - NURSING LAB & OFFICE	25-09
	DWG. NO.
	A-600


DATE	SCALE	DRAWN	CHECKED
2025.09.03	As indicated	MA	PC

NOTE: FURNITURE & EQUIPMENT
SHOWN FOR CONTEXT ONLY.

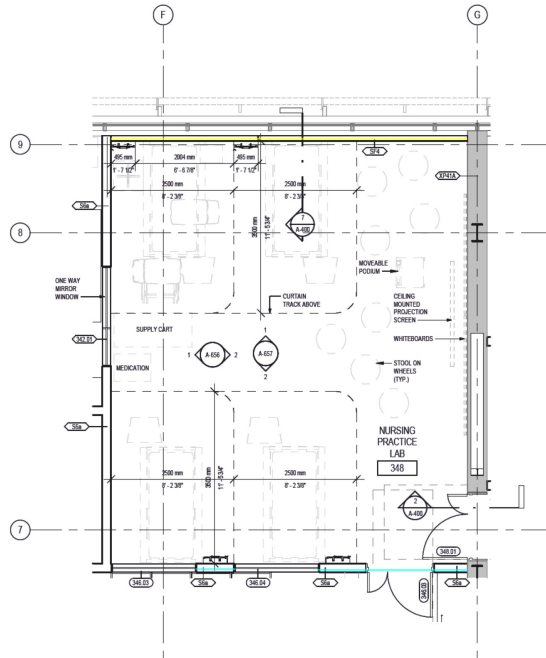


- S6a Wall (2780mm H)
- SF4 Wall (2780mm H)
- S6 Wall (2780mm H)

9.0 M
28.5 M
69.1 M

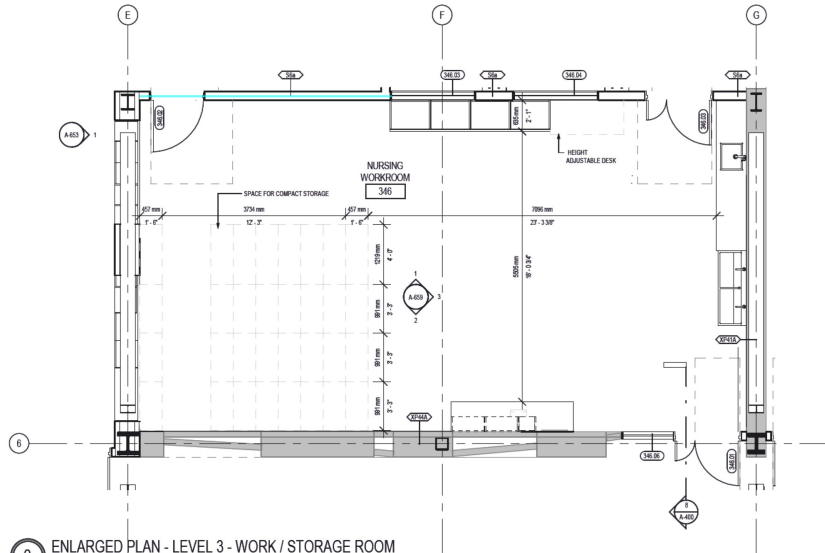

2 ENLARGED PLAN - LEVEL 3 - WORK / STORAGE ROOM
1:50

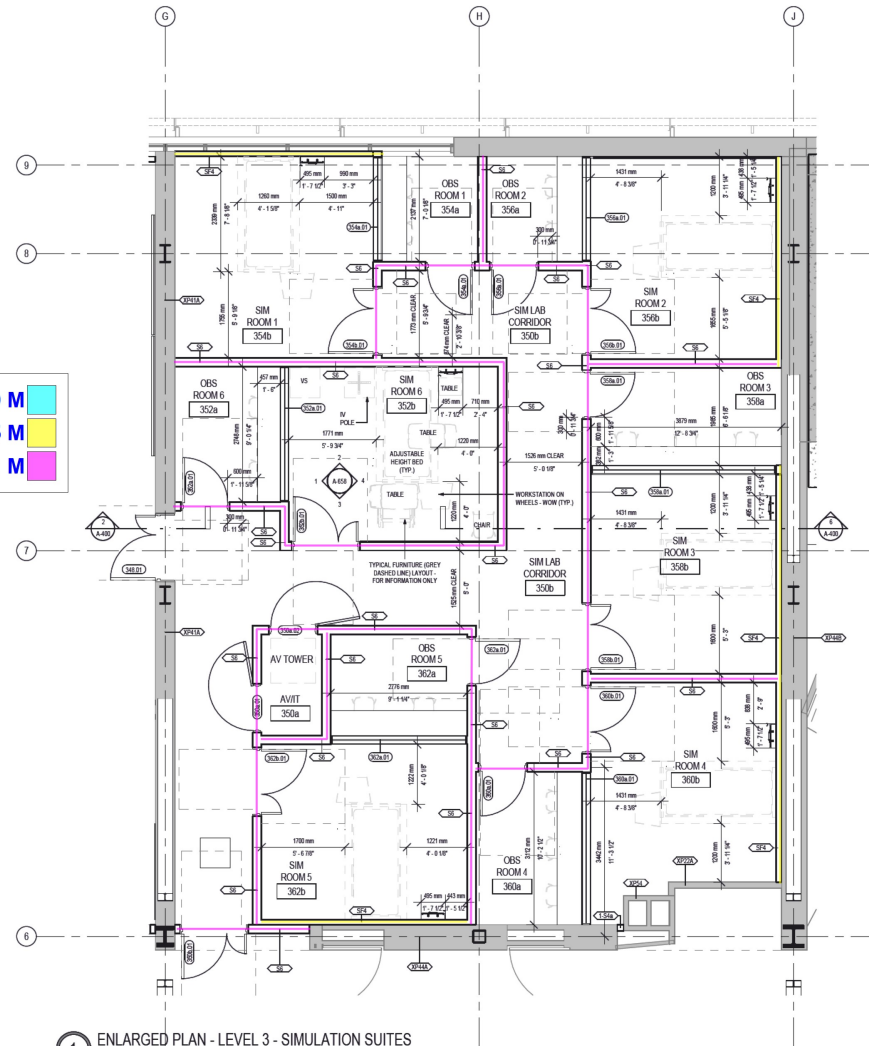

1 ENLARGED PLAN - LEVEL 3 - SIMULATION SUITES
1:50

(for Building Official's Use)

(for Certified Professional's Use)

KEY PLAN

ISSUED FOR TENDER	2025.12.05
ISSUED FOR BUILDING PERMIT	2025.09.17
ISSUED FOR BP DRAFT	2025.08.28

NO.	DESCRIPTION	BY	DATE
1	CLIENT REVISION		



PROJECT ADDRESS
170 W 49TH AVE, VANCOUVER BC

PROJECT
LANGARA NURSING EXPANSION
RENOVATION

DRAWING TITLE ENLARGED FLOOR PLANS - SIM SUITES, WORK ROOM & PRACTICE LAB	PROJECT NUMBER 25-09 DWG. NO. A-601
DATE 2025.09.03	SCALE As indicated
DRAWN M.A.	CHECKED P.C.